


南安市水头镇南侨村

(福建省泉州市鼎诚石材有限公司)

房
产
测
绘
报
告

泉州中科星桥空天技术有限公司

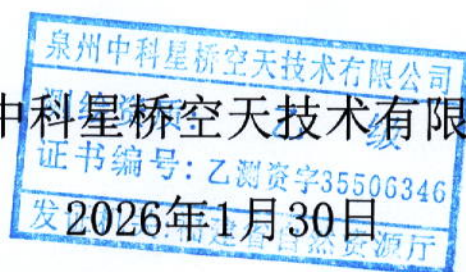


地址：安溪县龙门镇信息产业园众创基地6号楼

办公电话：15905976386 邮编：362442

监督电话：15905976386

目 录

1、房屋现状相片·····	1-12
2、宗地图·····	13
3、房屋现状平面图与房屋分层分户平面图·····	14
4、房屋面积测算汇总表·····	15
5、户室面积信息表·····	16
6、技术报告·····	17

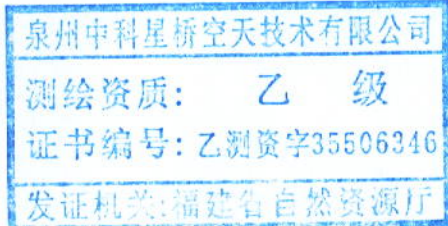



(1)

中国航空工业集团公司
中航工业集团
正：7200005000
发证机关：中国航空工业集团公司







泉州中科星桥空天技术有限公司

测绘资质：乙

证书编号: Z0000


发证机关

(2)

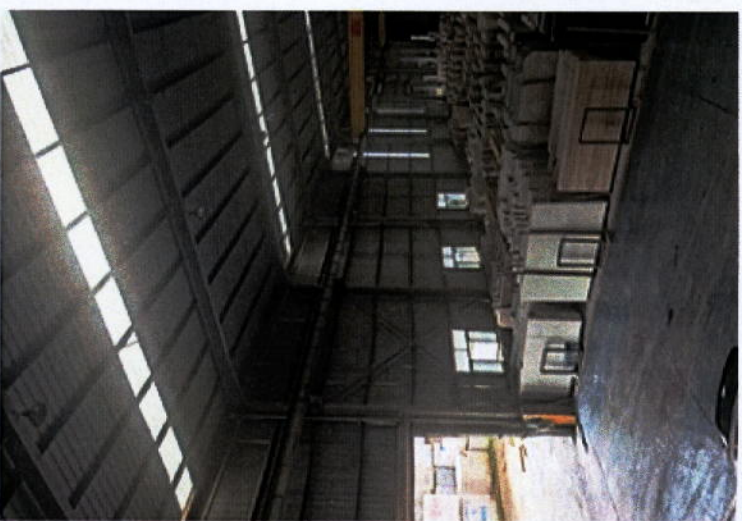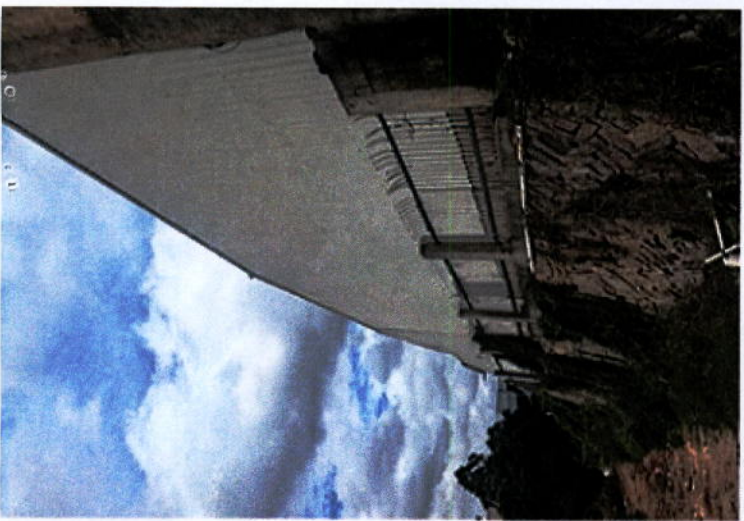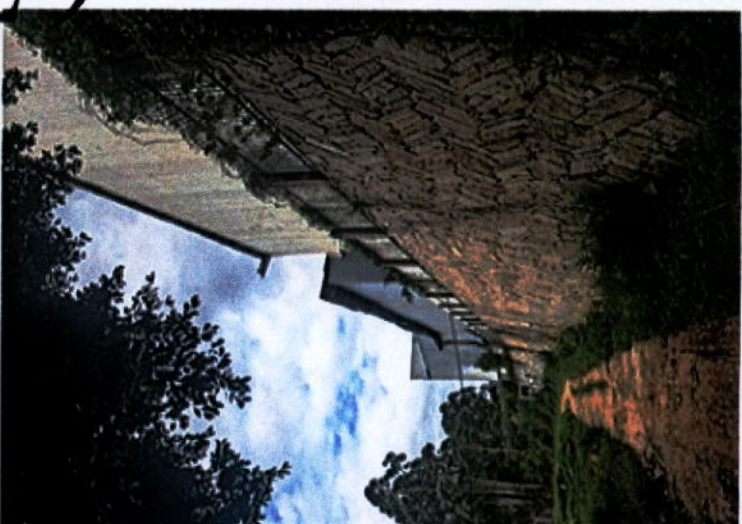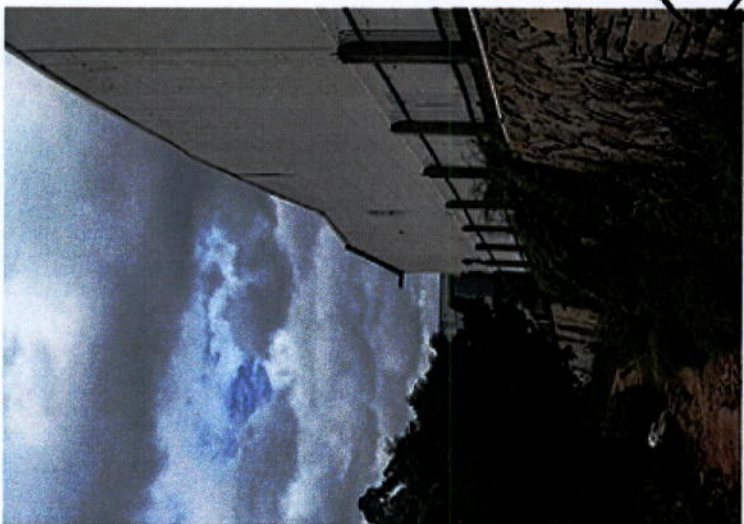



3

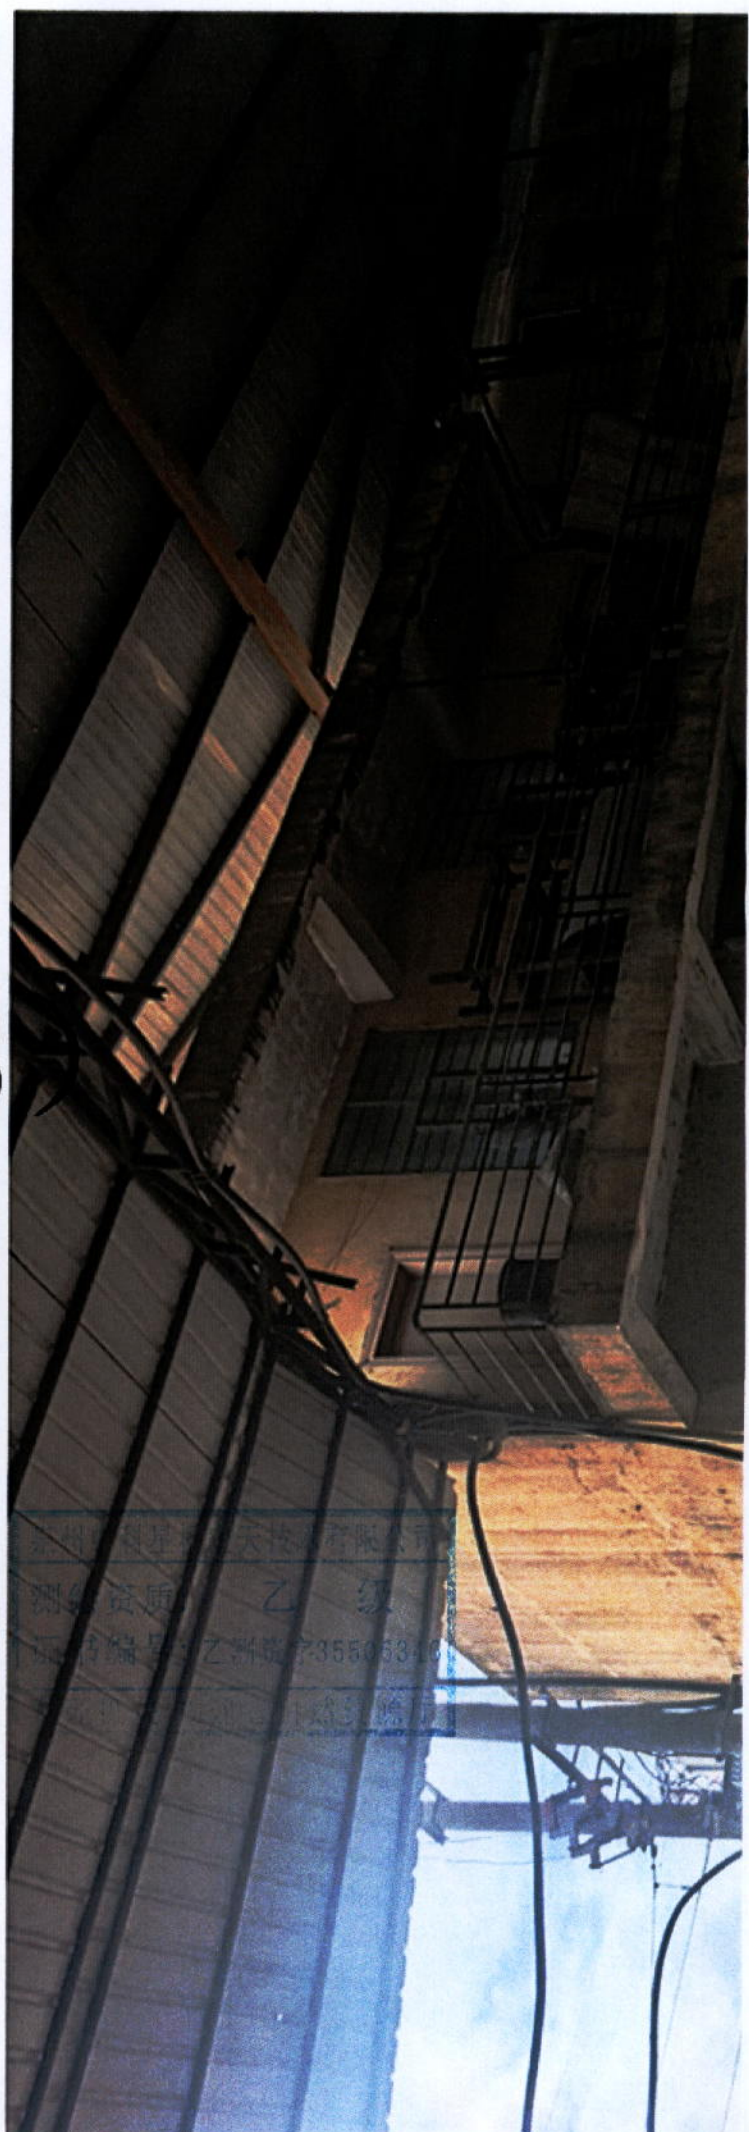



泉州中星建设工程有限公司


测绘资质 乙 级

证书编号: 乙测资字35506340

2023.06.01

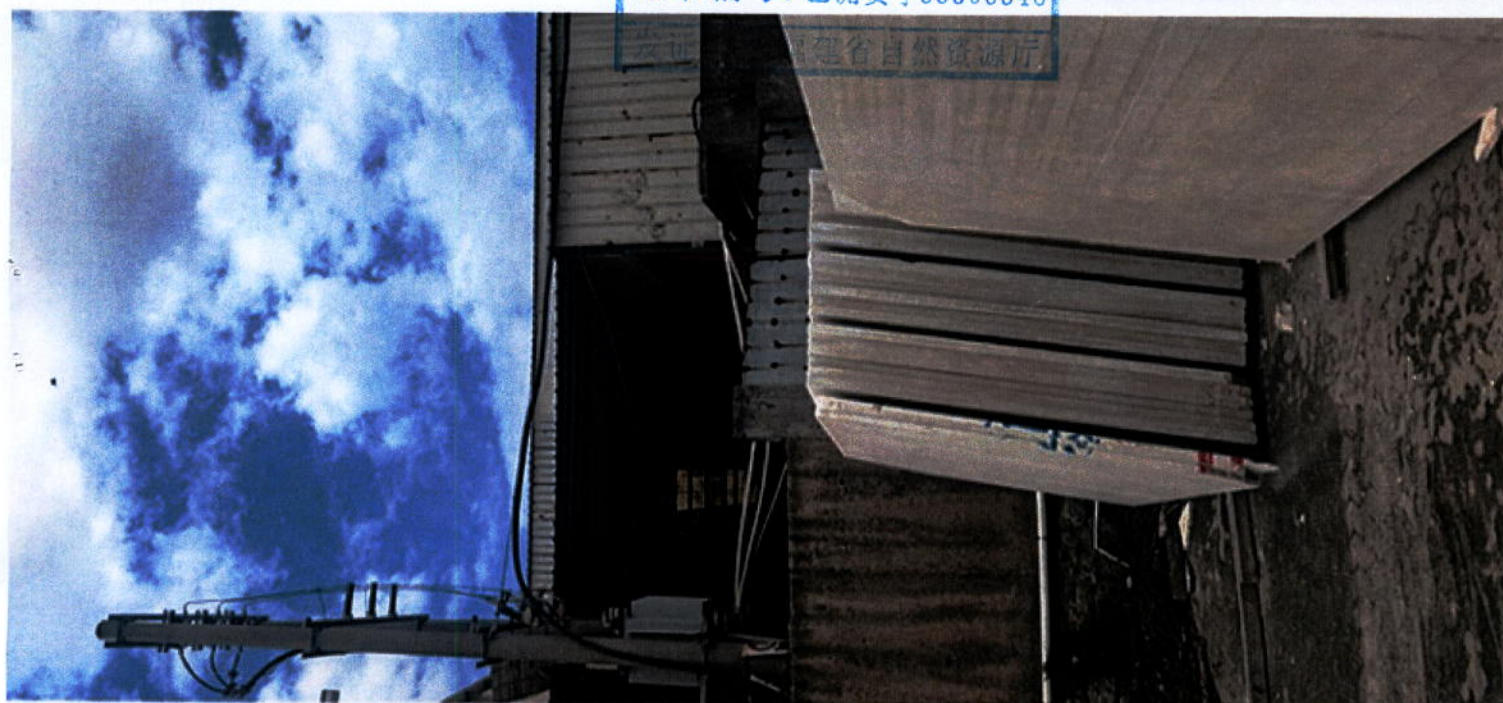


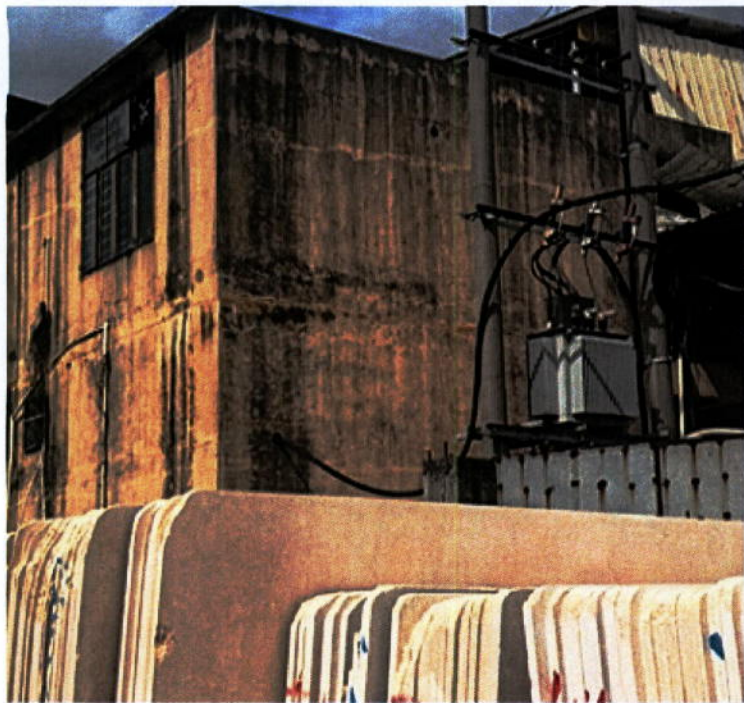


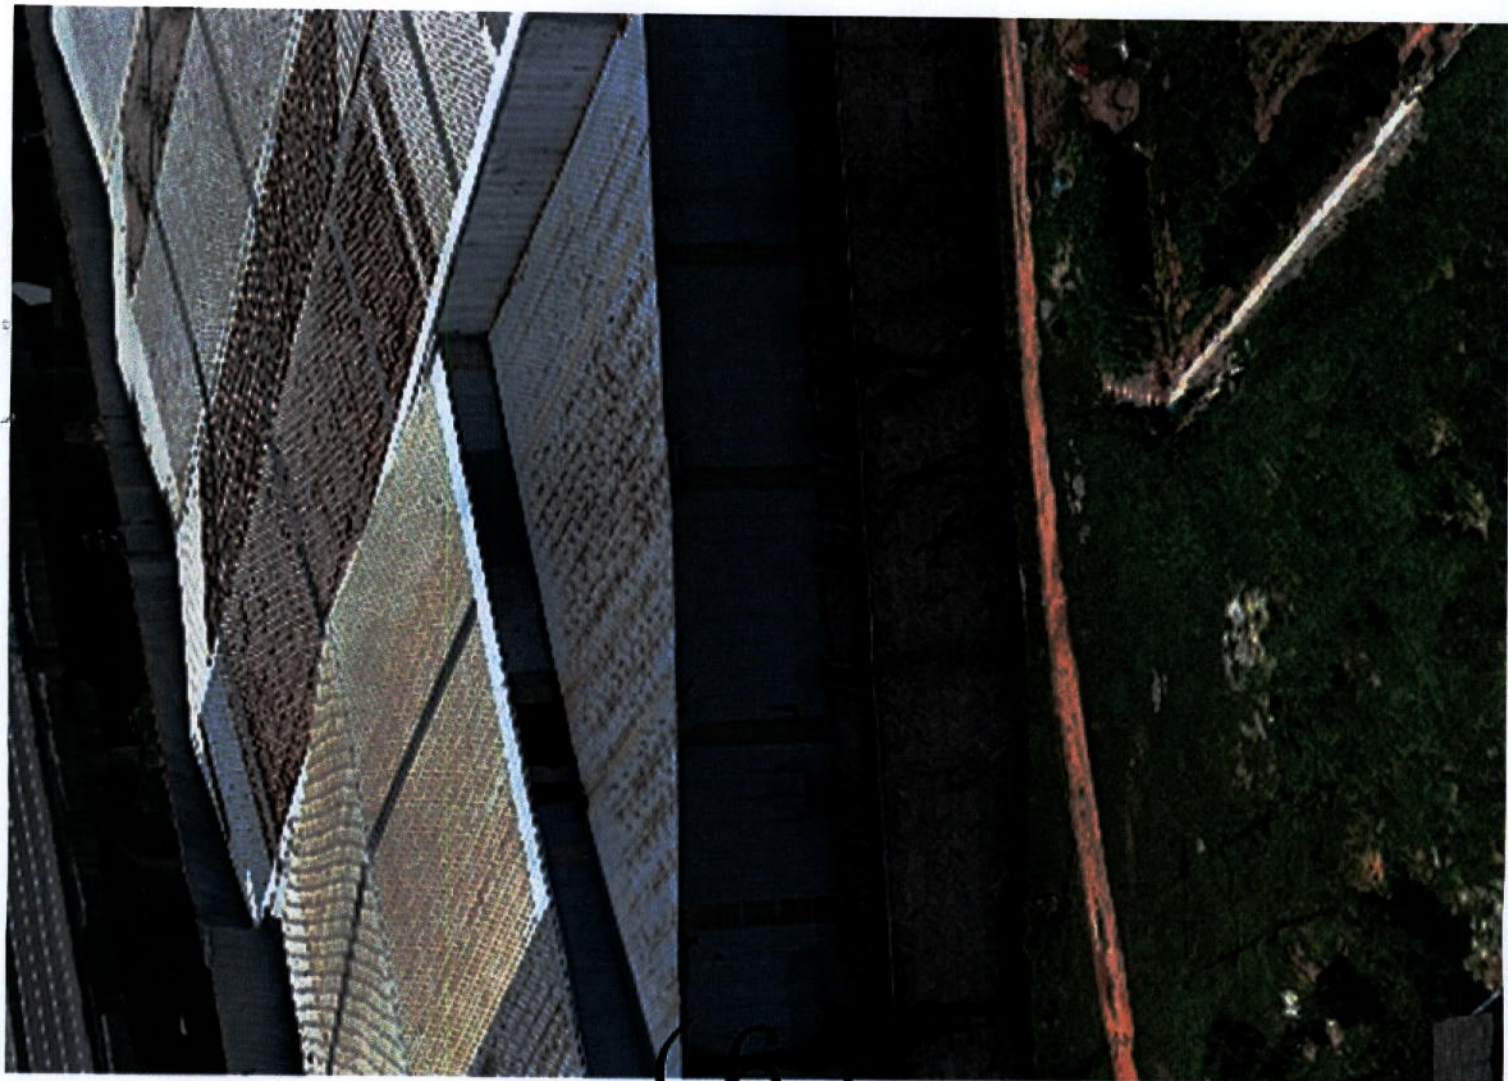




7

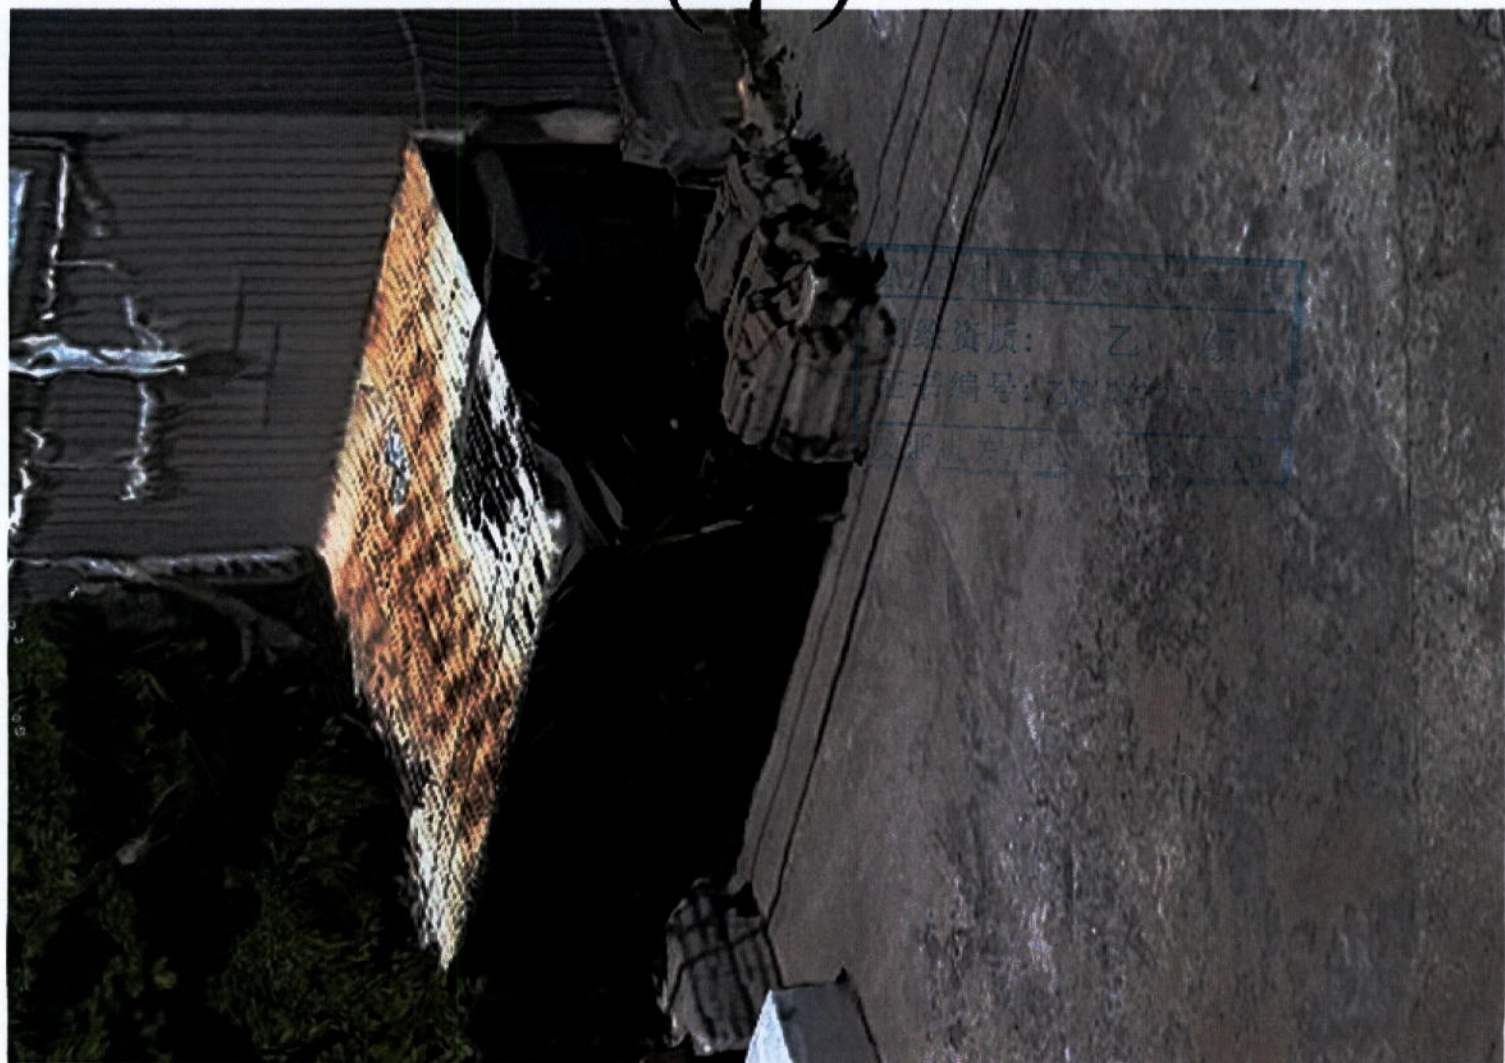

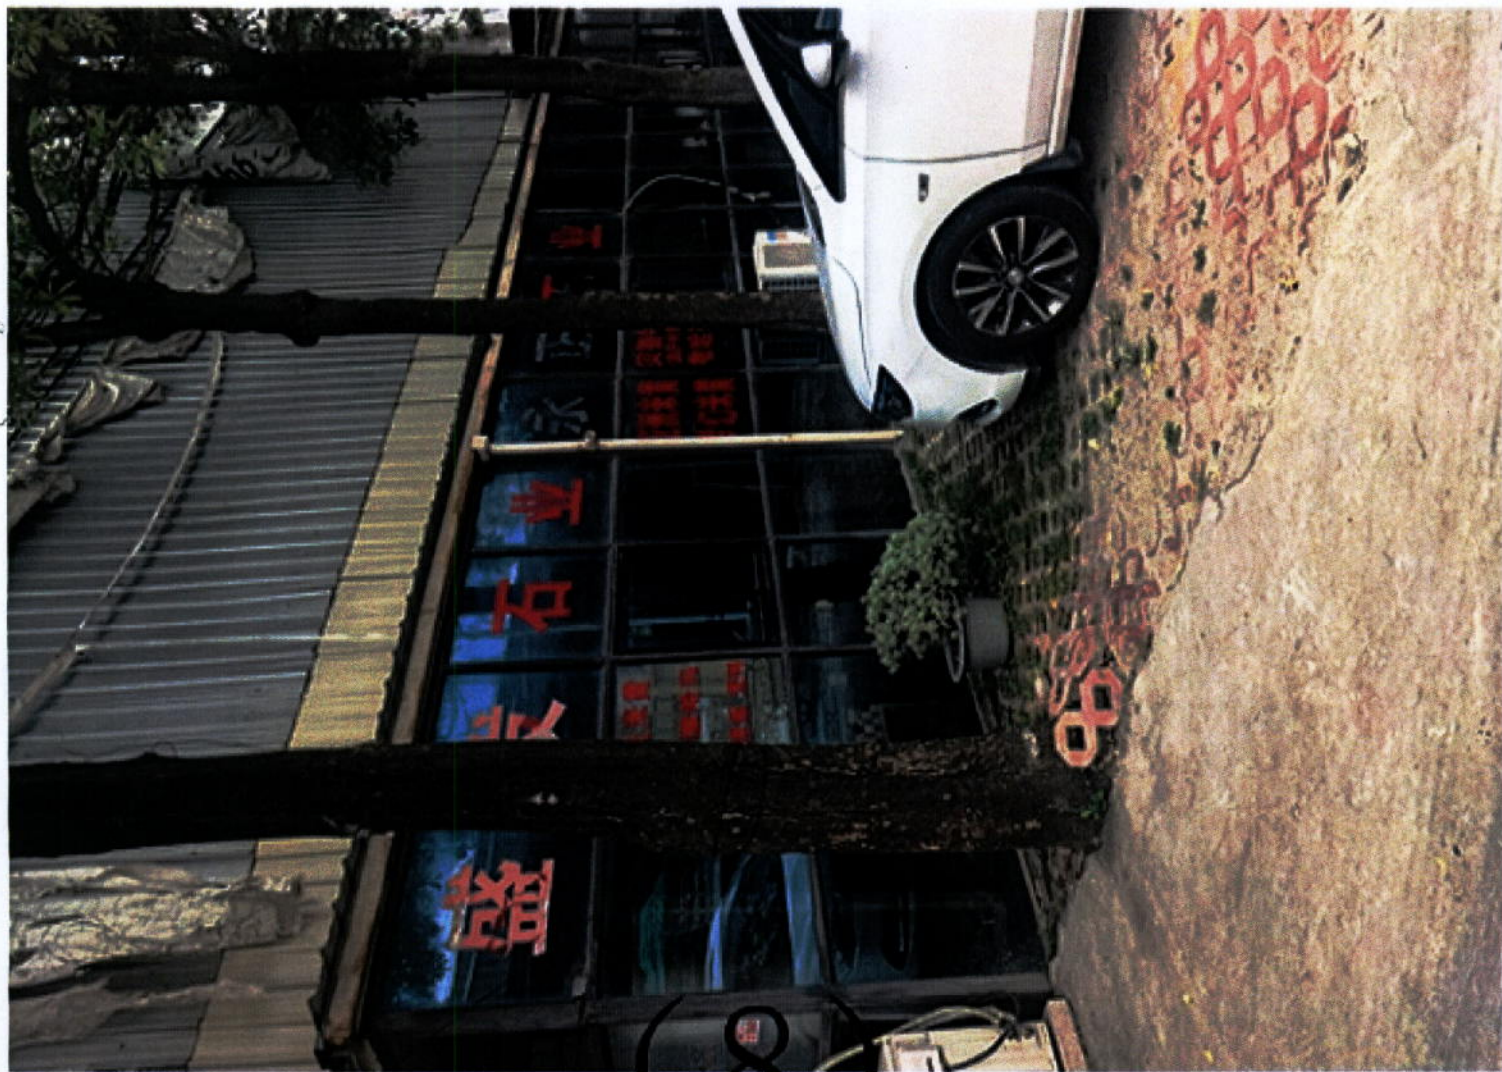



8





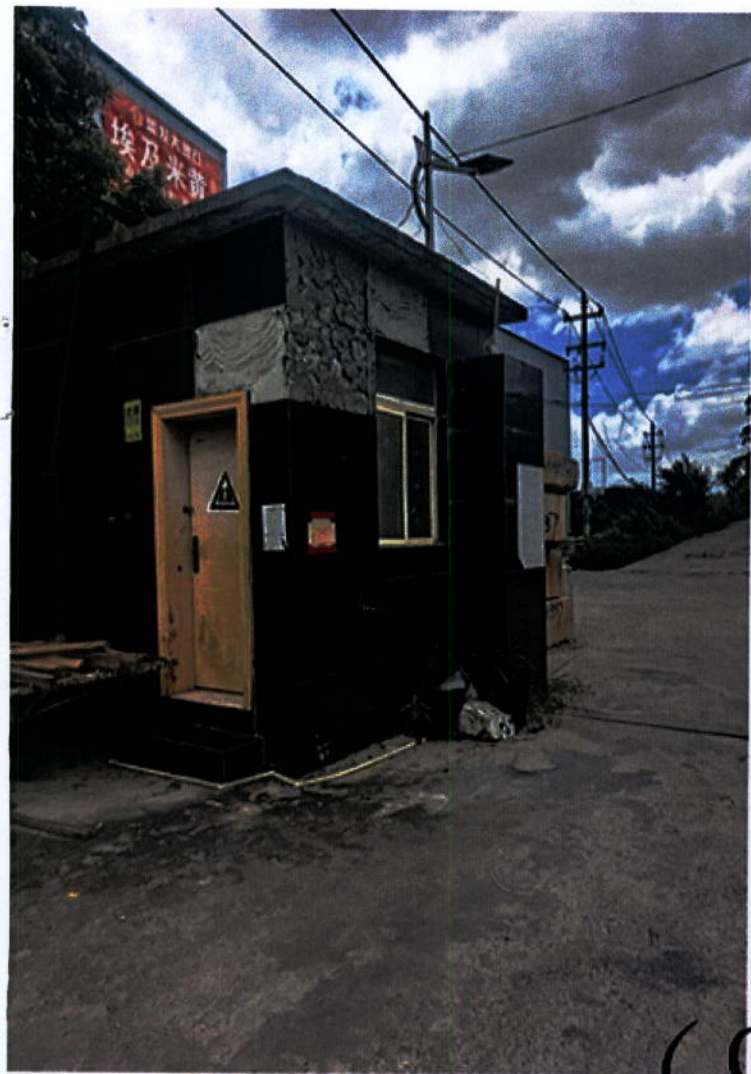


(9)



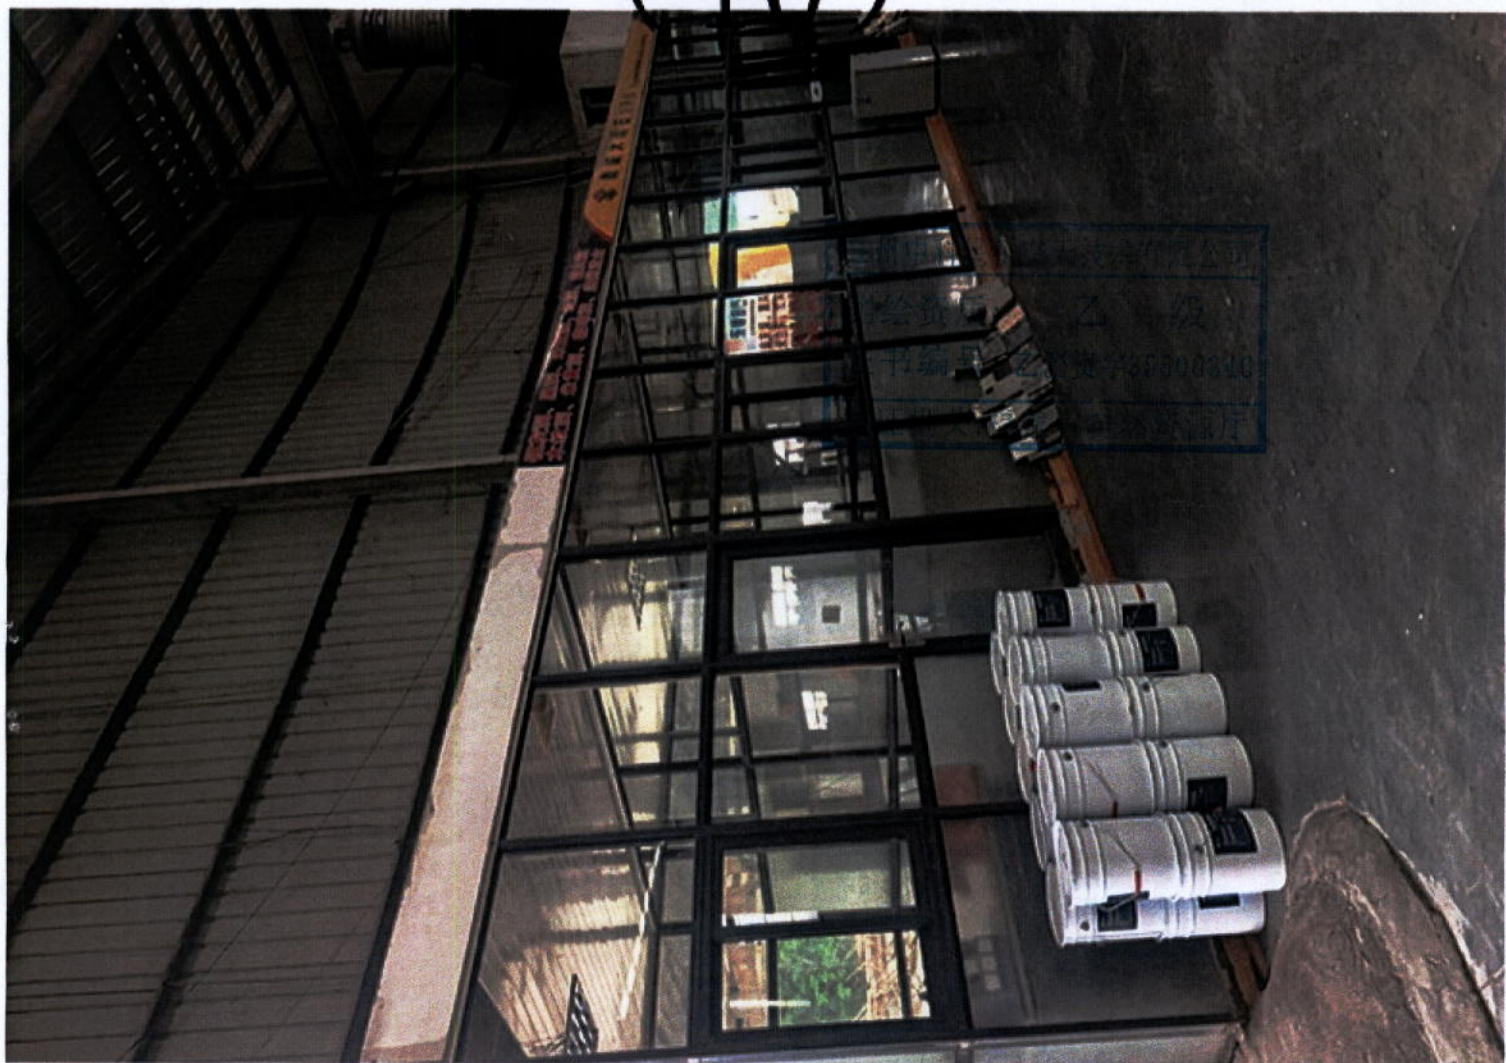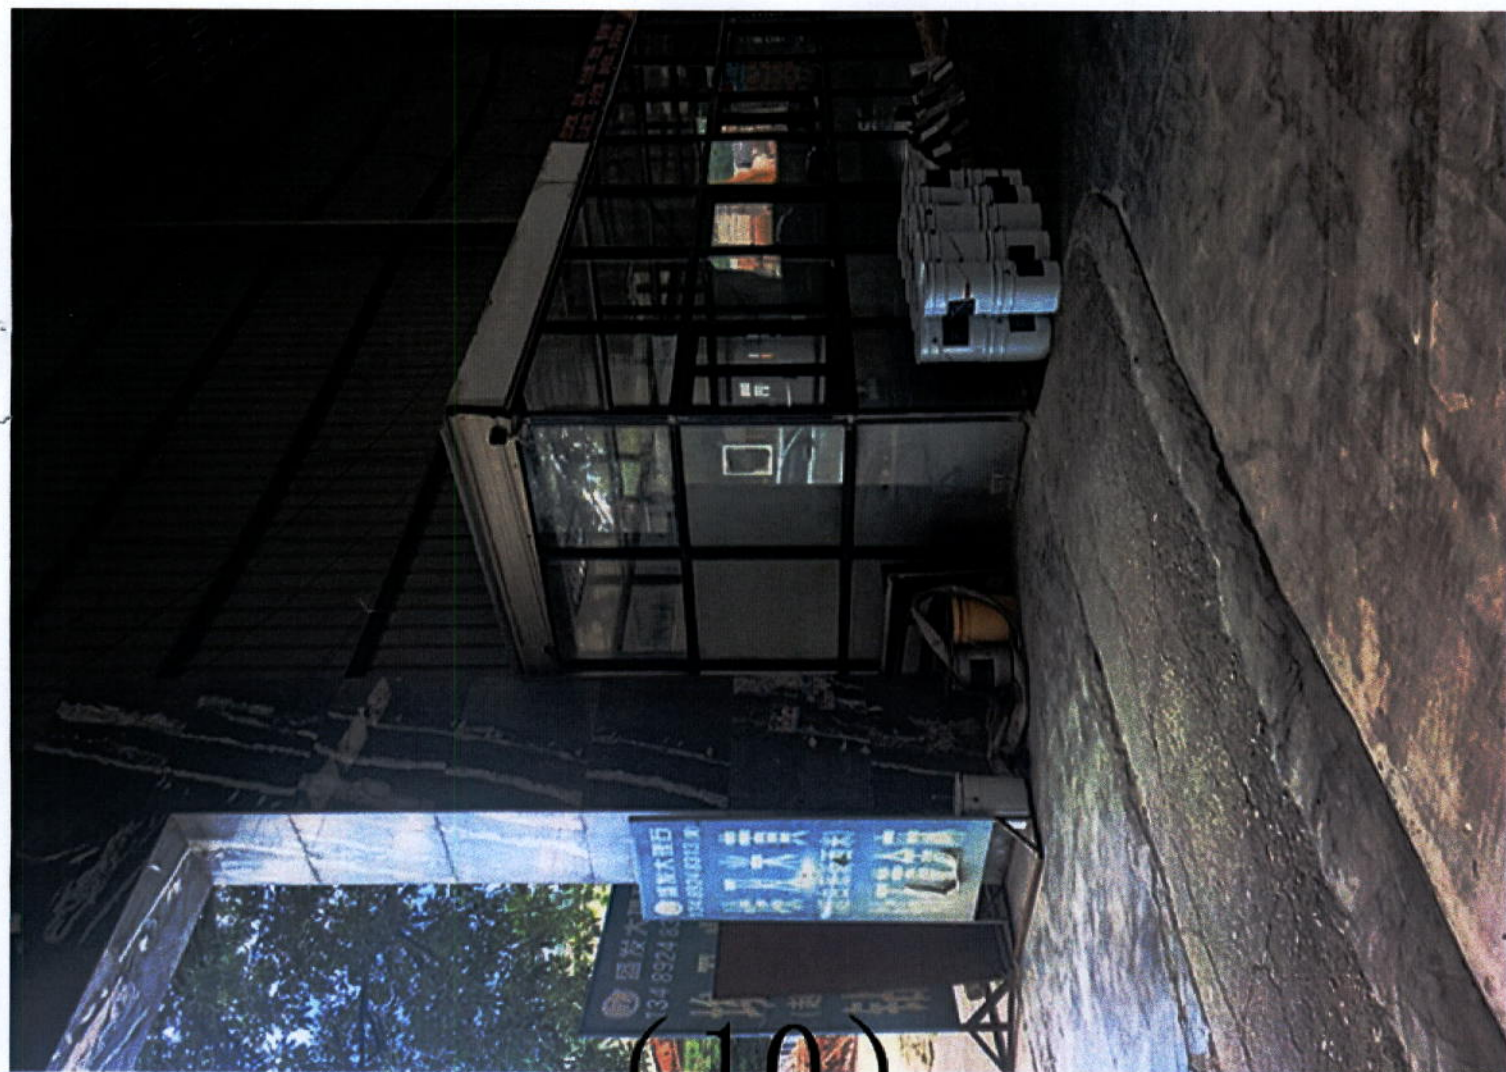

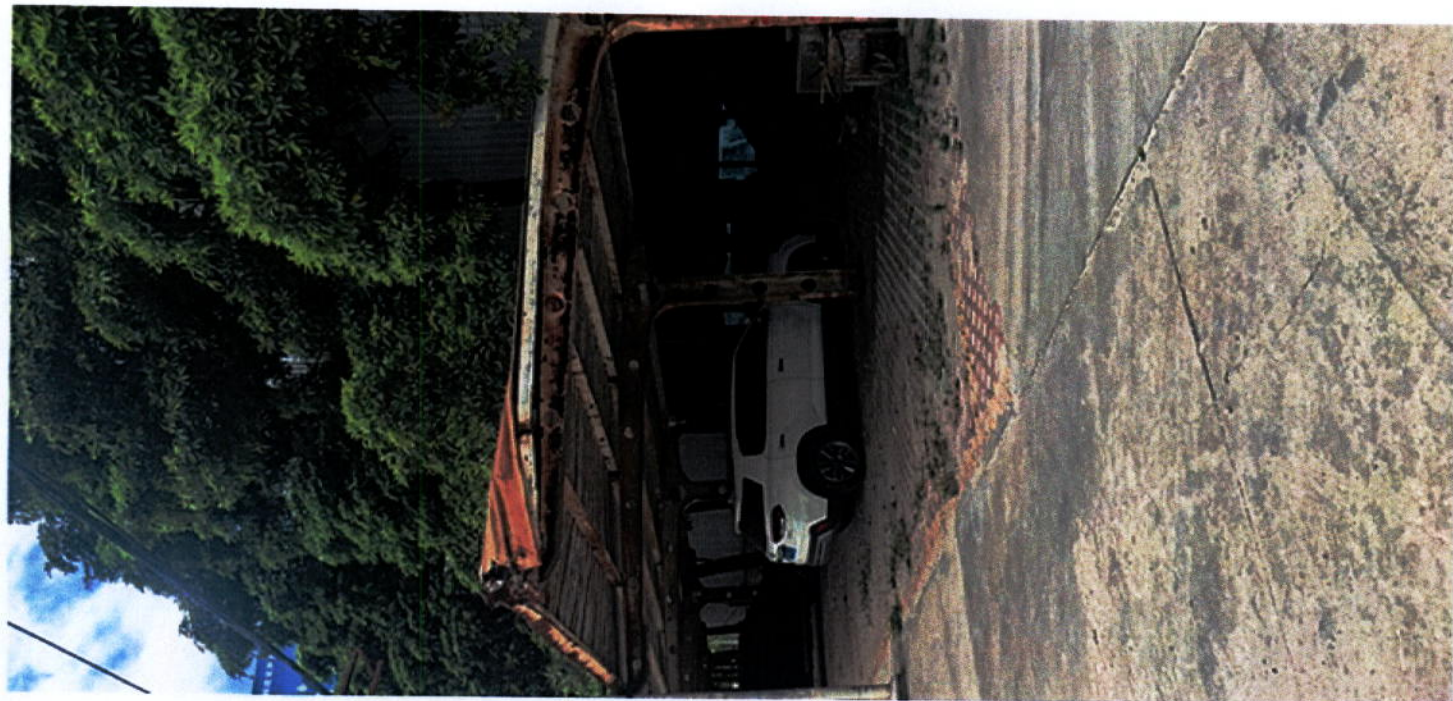

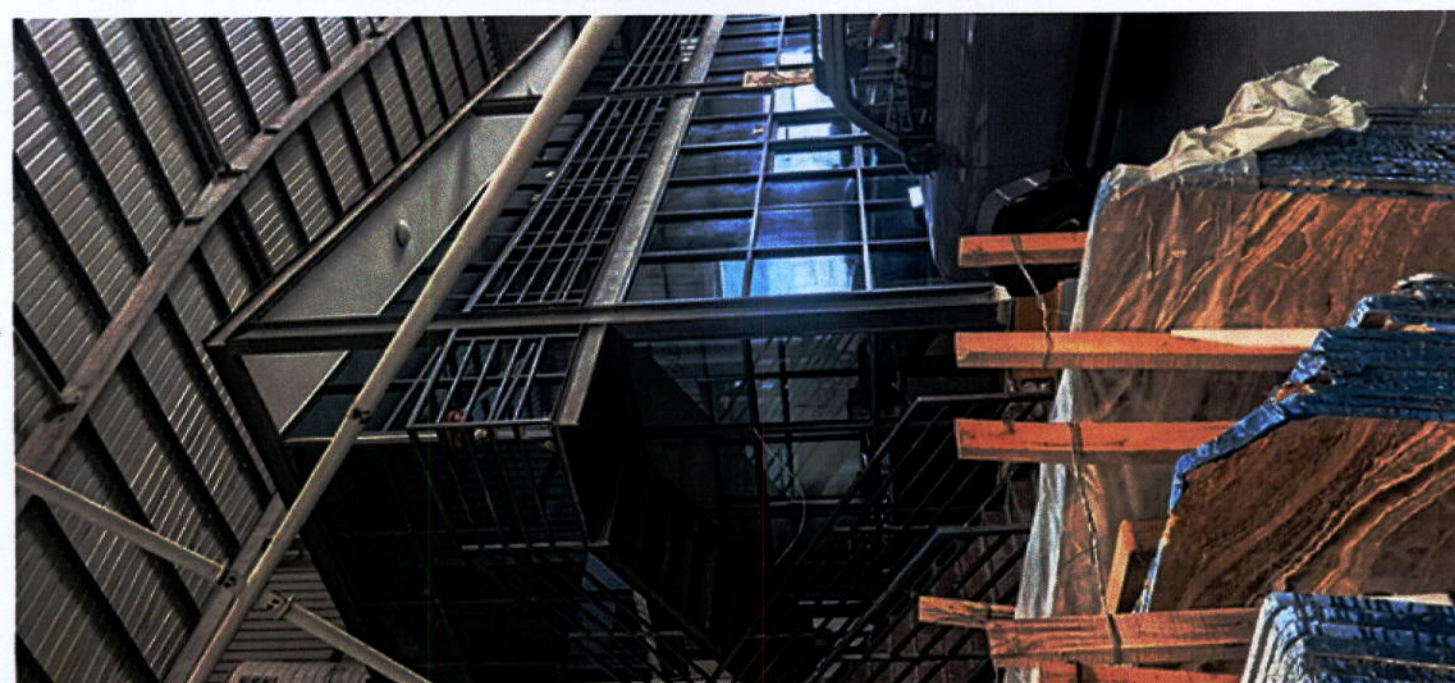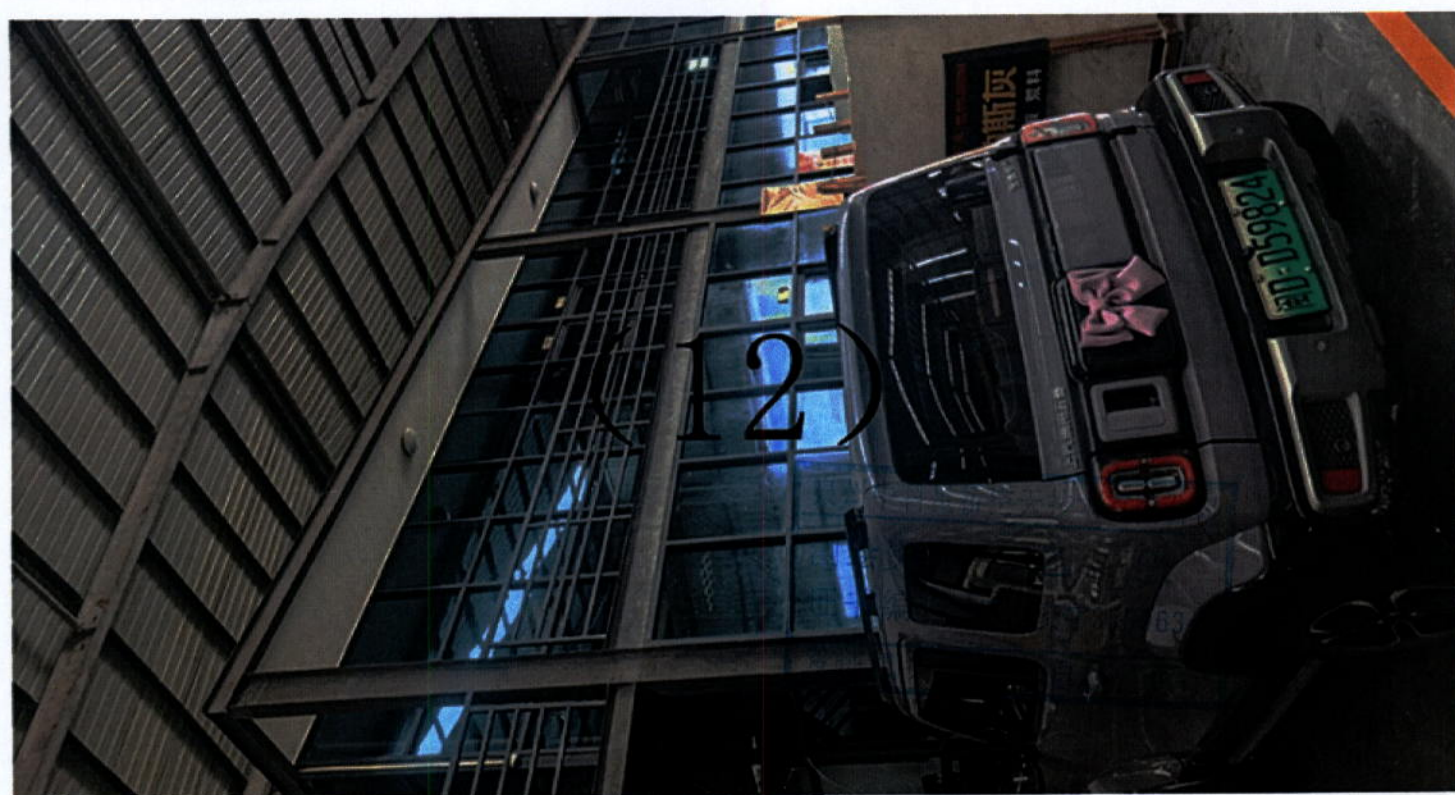


宗地图

单位: m² m

宗地面积: 21125

不动产单元号:

宗地坐落: 南安市水头镇南侨村

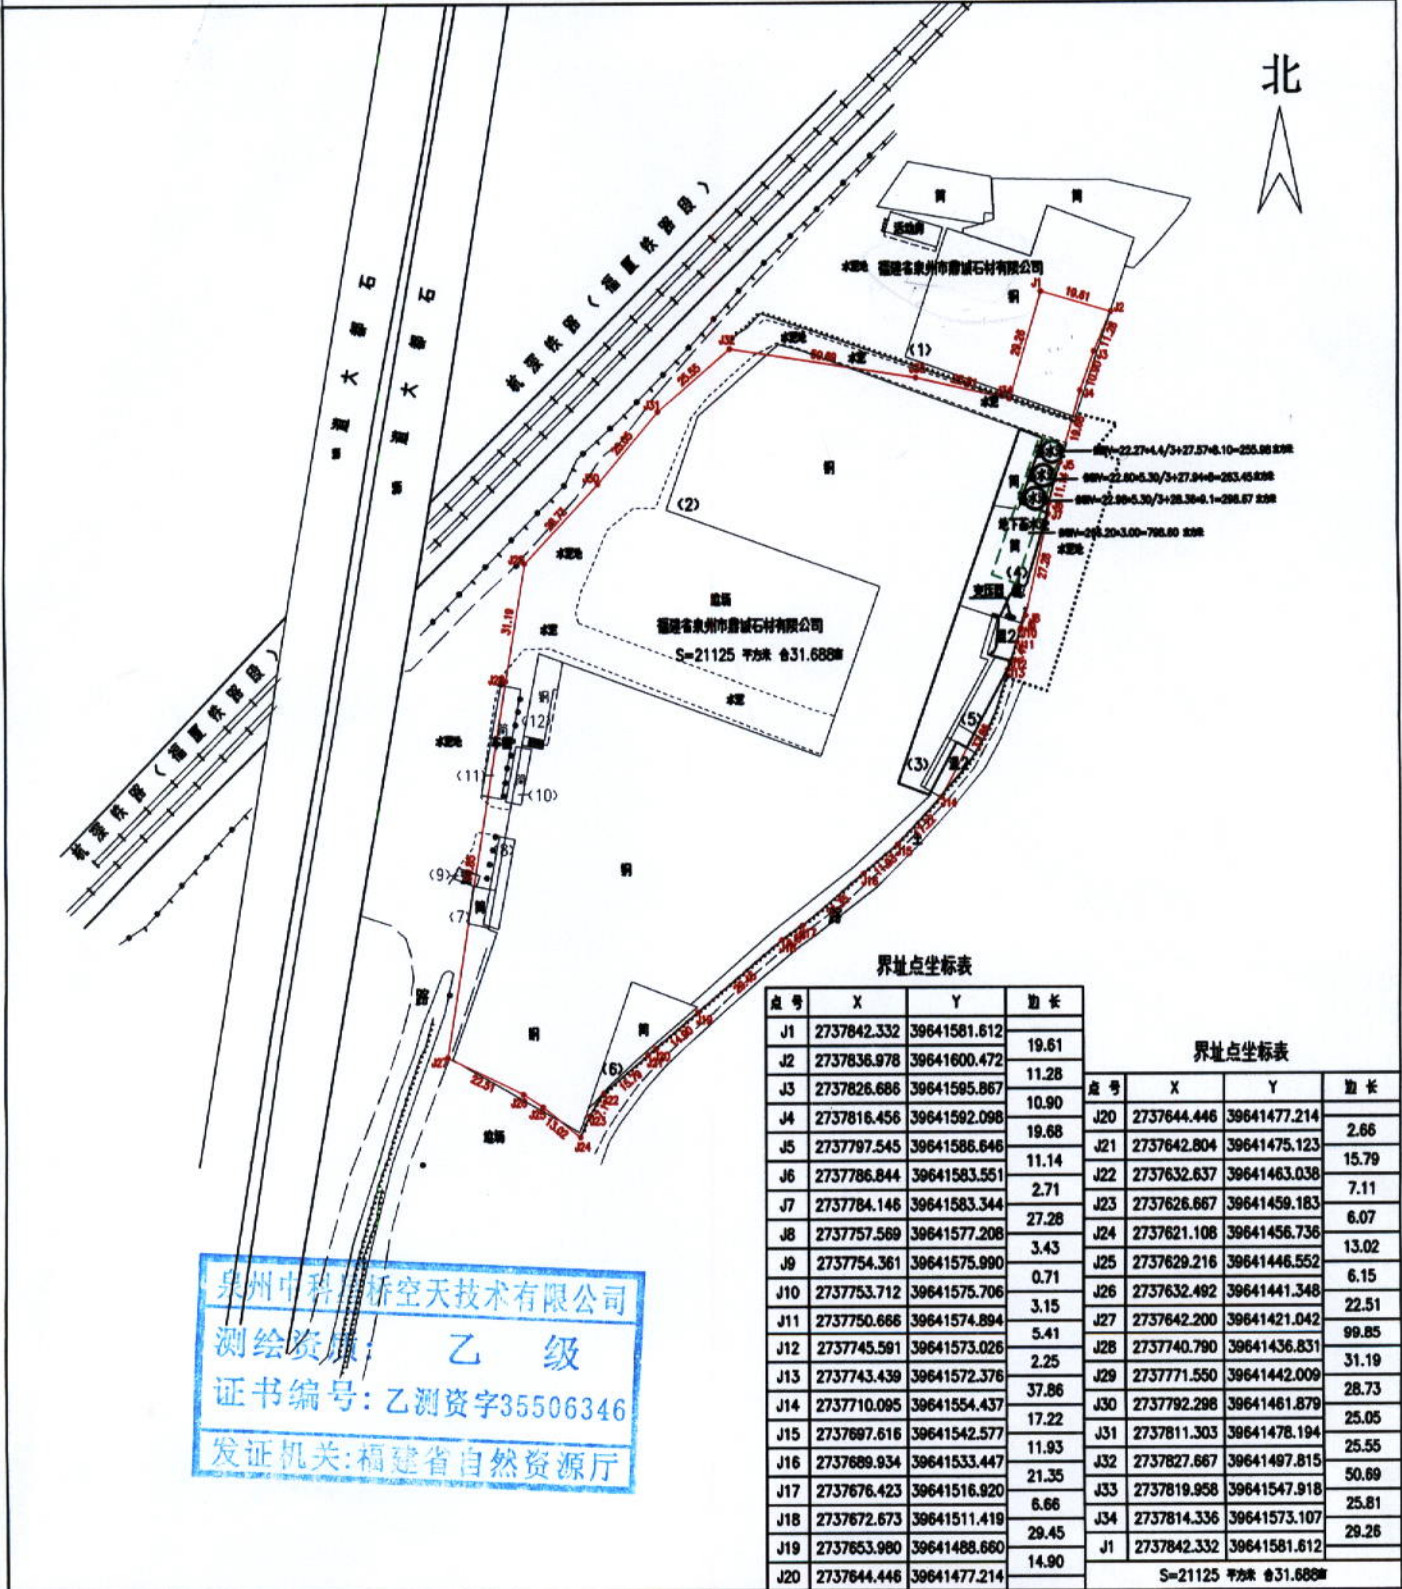


泉州中科星桥空天技术有限公司

西安80坐标系, L=117°
制图日期: 2026年1月30日
审核日期: 2026年1月30日

1:2000

测绘员: 黄志德
审核员: 林平


房屋现状平面图

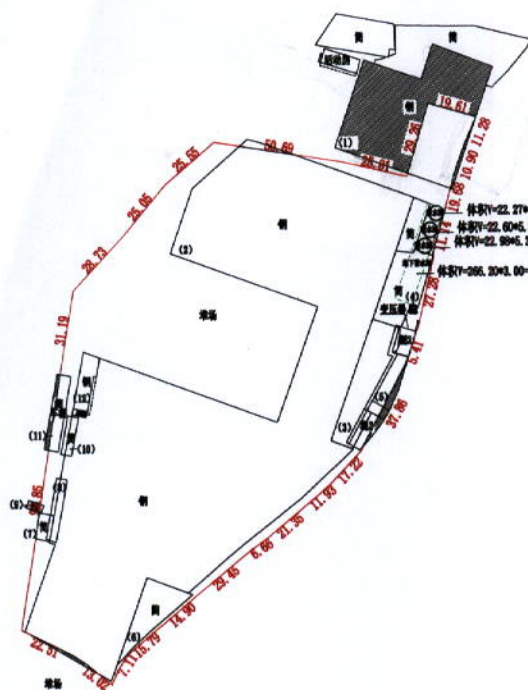


备注：阴影部分为红线外建筑面积部分

幢号	钢		混合		简易		合计
	红线内	红线外	红线内	红线外	红线内	红线外	
(1)	519.94	1565.00					2084.94
(2)	12757.89	56.52					12814.41
(3)					1221.75	44.92	1266.67
(4)			9.24				9.24
(5)			561.24	125.58			686.82
(6)					316.69		316.69
(7)					58.15		58.15
(8)					99.92		99.92
(9)			3.20	16.02			19.22
(10)					62.75		62.75
(11)					121.81	39.12	160.93
(12)	322.68						322.68
合计	13600.51	1621.52	573.68	141.60	1881.07	84.04	17902.42


房屋分层分户平面图

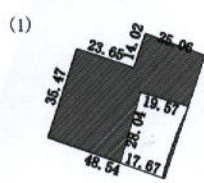


一层
面积计算：S=519.94
S=1565.00 阴影部分

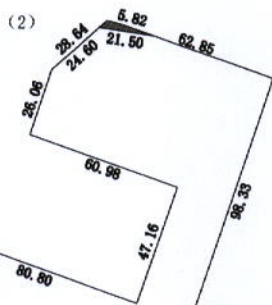


一层
面积计算：S=12757.89
S=56.52 阴影部分

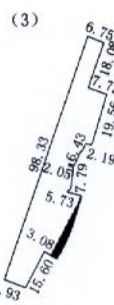


一层
面积计算：S=1221.75
S=44.92

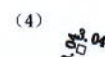


一层
面积计算：S=9.24

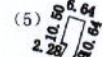

面积计算：S=264.13
S=62.79 阴影部分

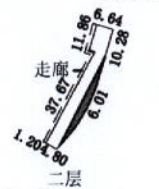

二层
面积计算：S=297.11
S=62.79 阴影部分

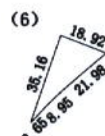

一层
面积计算：S=316.69




一层
面积计算：S=58.15




一层
面积计算：S=99.92




一层
面积计算：S=3.20
S=16.02 阴影部分

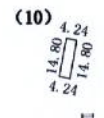

一层
面积计算：S=62.75

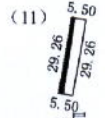

面积计算：S=121.81
S=39.12 阴影部分

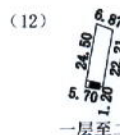

一层至二层
面积计算：S=161.34
S*2=322.68

泉州中科星桥空天技术有限公司

测绘资质：乙级

证书编号：乙测资字35506346

泉州中科星桥空天技术有限公司

座 落	南安市水头镇南侨村			幢 号	(1)、(2)、(3)、(4)、(5)、(6)、(7)、(8)、(9)、(10)、(11)、(12)	套内建筑面积	㎡
产权人	福建省泉州市鼎诚石材有限公司			层 数	1层、1层、1层、1层、2层、1层、1层、1层、1层、1层、2层	共有分摊面积	㎡
共有权人		占地面积	15596.81㎡	层 次	1-1层、1-1层、1-1层、1-1层、1-2层、1-1层、1-1层、1-1层、1-1层、1-1层、1-1层、1-2层	建 筑 面 积	17902.42㎡
用 途	工业	用地面积	21125 ㎡	结 构	钢、钢、简易、混合、混合、简易、简易、简易、混合、简易、简易、钢	比 例 尺	1:3000

测量员：林平、黄志德

绘图员：林平

房屋面积测算汇总表

面积单位: m² 第15页

产权人:		福建省泉州市鼎诚石材有限公司						
房屋座落:		南安市水头镇南侨村						
土地证编号:								
宗地面积		21125	宗地内 总建筑占地		15596.81	总建筑 面 积	17902.42	
幢号	幢名	基本 用途	结构	层数	本幢建筑 占地面积	本幢建筑 面 积	建成年份	备注
(1)		工业	钢	1	519.94	2084.94	已建多年	
(2)		工业	钢	1	12757.89	12814.41	已建多年	
(3)		工业	简易	1	1221.75	1266.67	已建多年	
(4)		工业	混合	1	9.24	9.24	已建多年	
(5)		工业	混合	2	264.13	686.82	已建多年	
(6)		工业	简易	1	316.69	316.69	已建多年	
(7)		工业	简易	1	58.15	58.15	已建多年	
(8)		工业	简易	1	99.92	99.92	已建多年	
(9)		工业	混合	1	3.20	19.22	已建多年	
(10)		工业	简易	1	62.75	62.75	已建多年	
(11)		工业	简易	1	121.81	160.93	已建多年	
(12)		工业	钢	2	161.34	322.68	已建多年	
合 计:					15596.81	17902.42		
说 明:		水池总体积V=1616.70立方米						

计算者:黄志德

检查者 林平

户室面积信息表

面积单位: m² 第16页

产 权 人:	福建省泉州市鼎诚石材有限公司				幢 数:	12
房屋座落:	南安市水头镇南侨村				总建筑面积:	17902.42
幢 号	层 次	层建筑面积	层阴影建筑面积	本幢建筑面积合计	产 别	备注:
(1)	1	519.94	1565.00	2084.94	私有	
(2)	1	12757.89	56.52	12814.41	私有	
(3)	1	1221.75	44.92	1266.67	私有	
(4)	1	9.24	0.00	9.24	私有	
(5)	1	264.13	62.79	686.82	私有	
	2	297.11	62.79			
(6)	1	316.69	0.00	316.69	私有	
(7)	1	58.15	0.00	58.15	私有	
(8)	1	99.92	0.00	99.92	私有	
(9)	1	3.20	16.02	19.22	私有	
(10)	1	62.75	0.00	62.75	私有	
(11)	1	121.81	39.12	160.93	私有	
(12)	1	161.34	0.00	322.68	私有	
	2	161.34	0.00			
合计		16055.26	1847.16	17902.42		
说明:						

填表者: 黄志德

检查者: 林平

